


TOPOGRAPHIC SURVEY PLAN OF PROPOSED DEVELOPMENT SITE

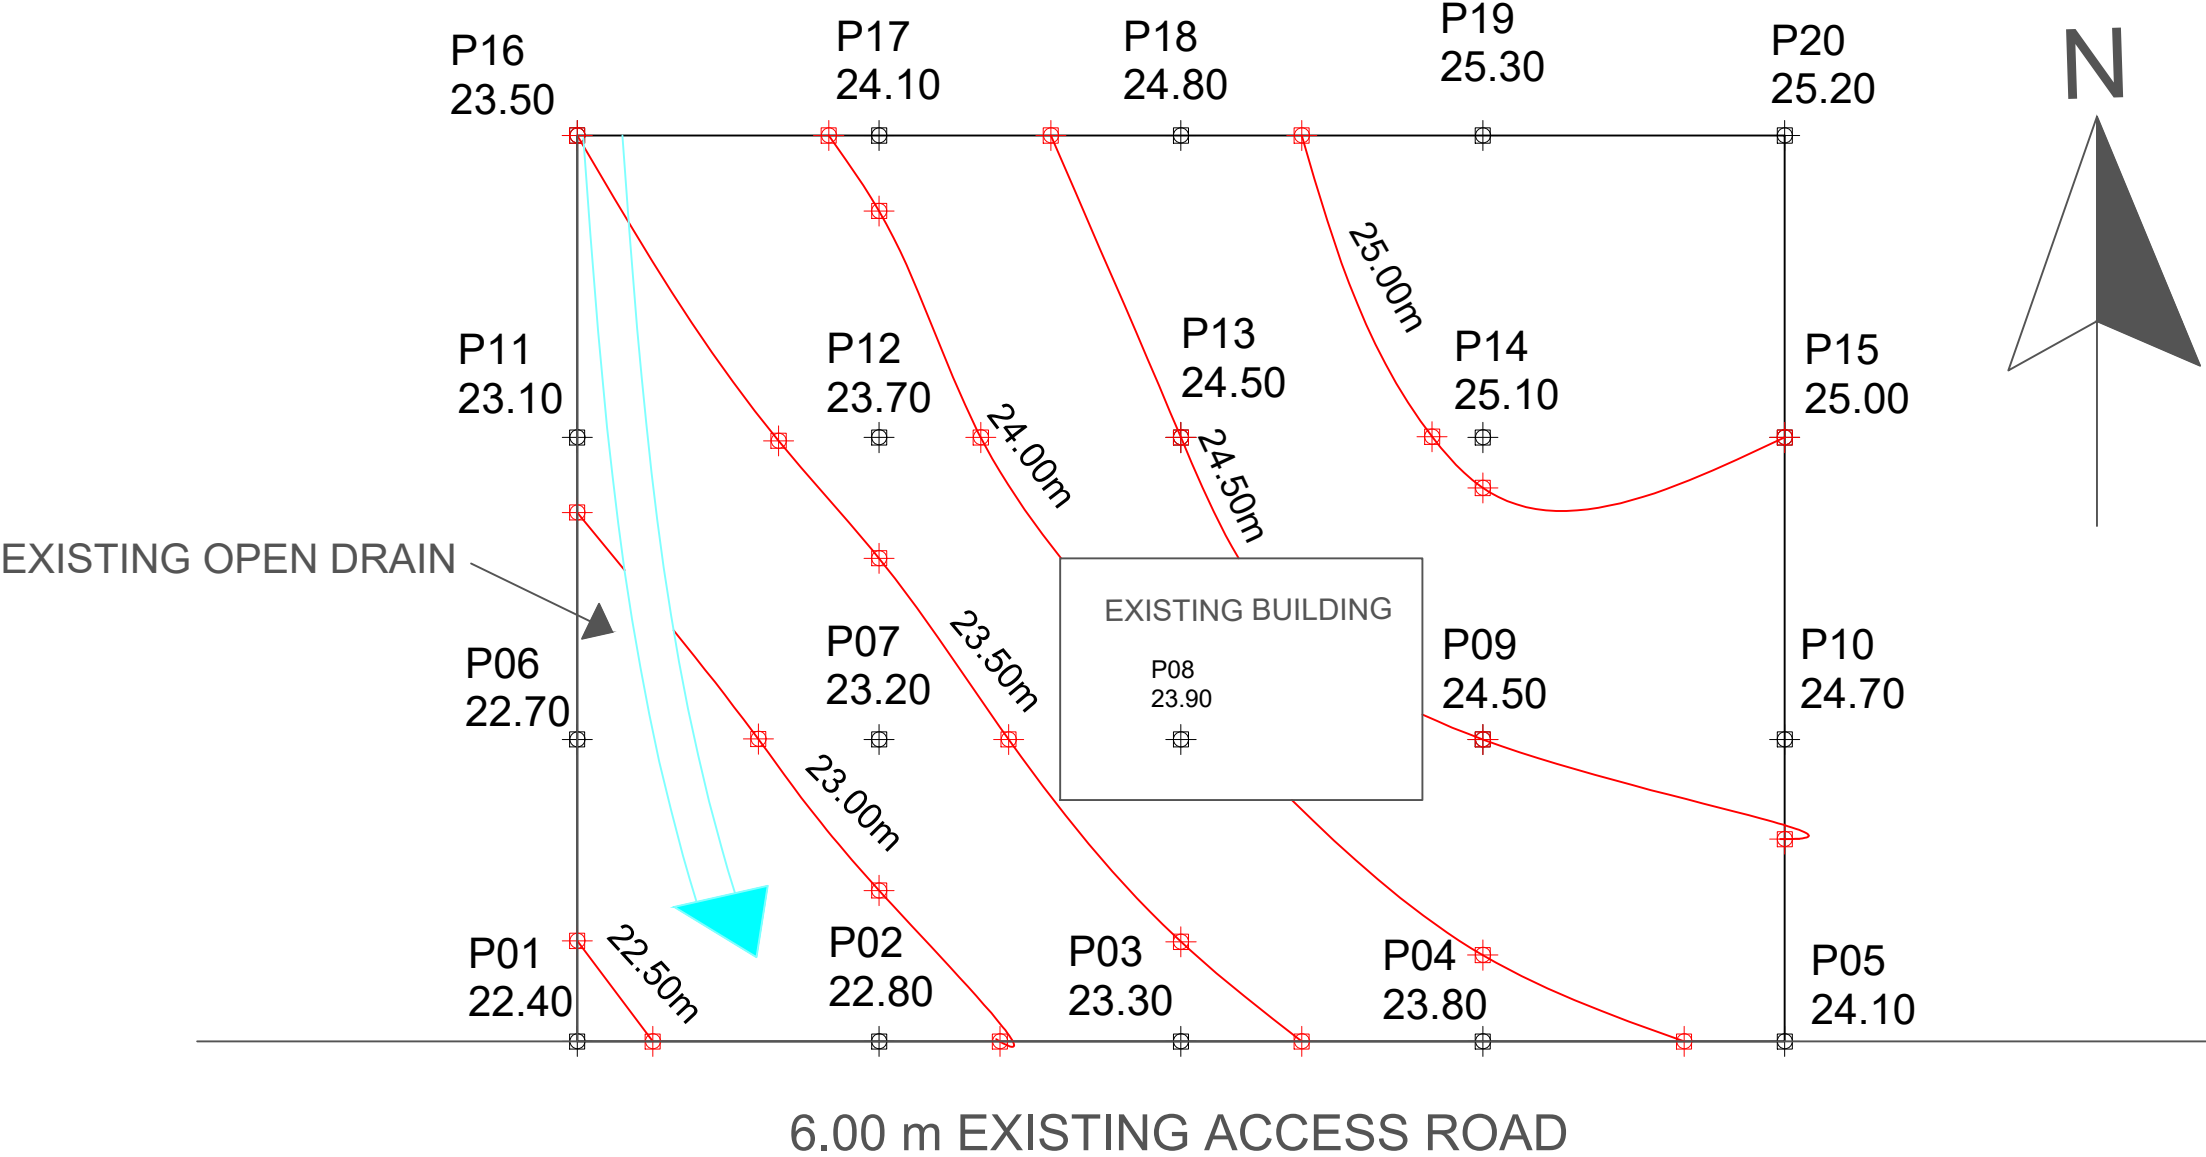

NOTES:

- 1. All dimensions and elevations are in metres.
- 2. Contour interval = 0.50 m.
- 3. Elevations shown are simulated spot heights.
- 4. Contours were interpolated from spot-height data.
- 5. Existing site features are shown for reference.
- 6. Drawing prepared for educational and portfolio purposes only.

LEGEND

- Site Boundary
- ~~~~~ Contour Line
- + Survey / Spot Height Point
- Existing Building
- ==== Existing Access Road
- > Existing Open Drain / Flow Direction

PROJECT:

Proposed Development Site

DRAWING:

Topographic Survey Plan

DRAWN BY:

Olaribigbe OLamposi

SCALE:

1:500

DATE:

September 2026